
# 2-ACRE MORINGA IRRIGATION — MASTER BLUEPRINT

SHEET 1 OF 2 : TOP-DOWN MASTER FIELD BLUEPRINT

PLOT A RISER = 4' 2" RISER + 2x 50MM BALL VALVES + 15' N/S 1.5" SUBLINES + 2x 50MM FLUSH VALVES

PLOT B RISER = 4' 2" RISER + 2x 40MM BALL VALVES + 32' N/S 1.25" SUBLINES + 2x 40MM FLUSH VALVES

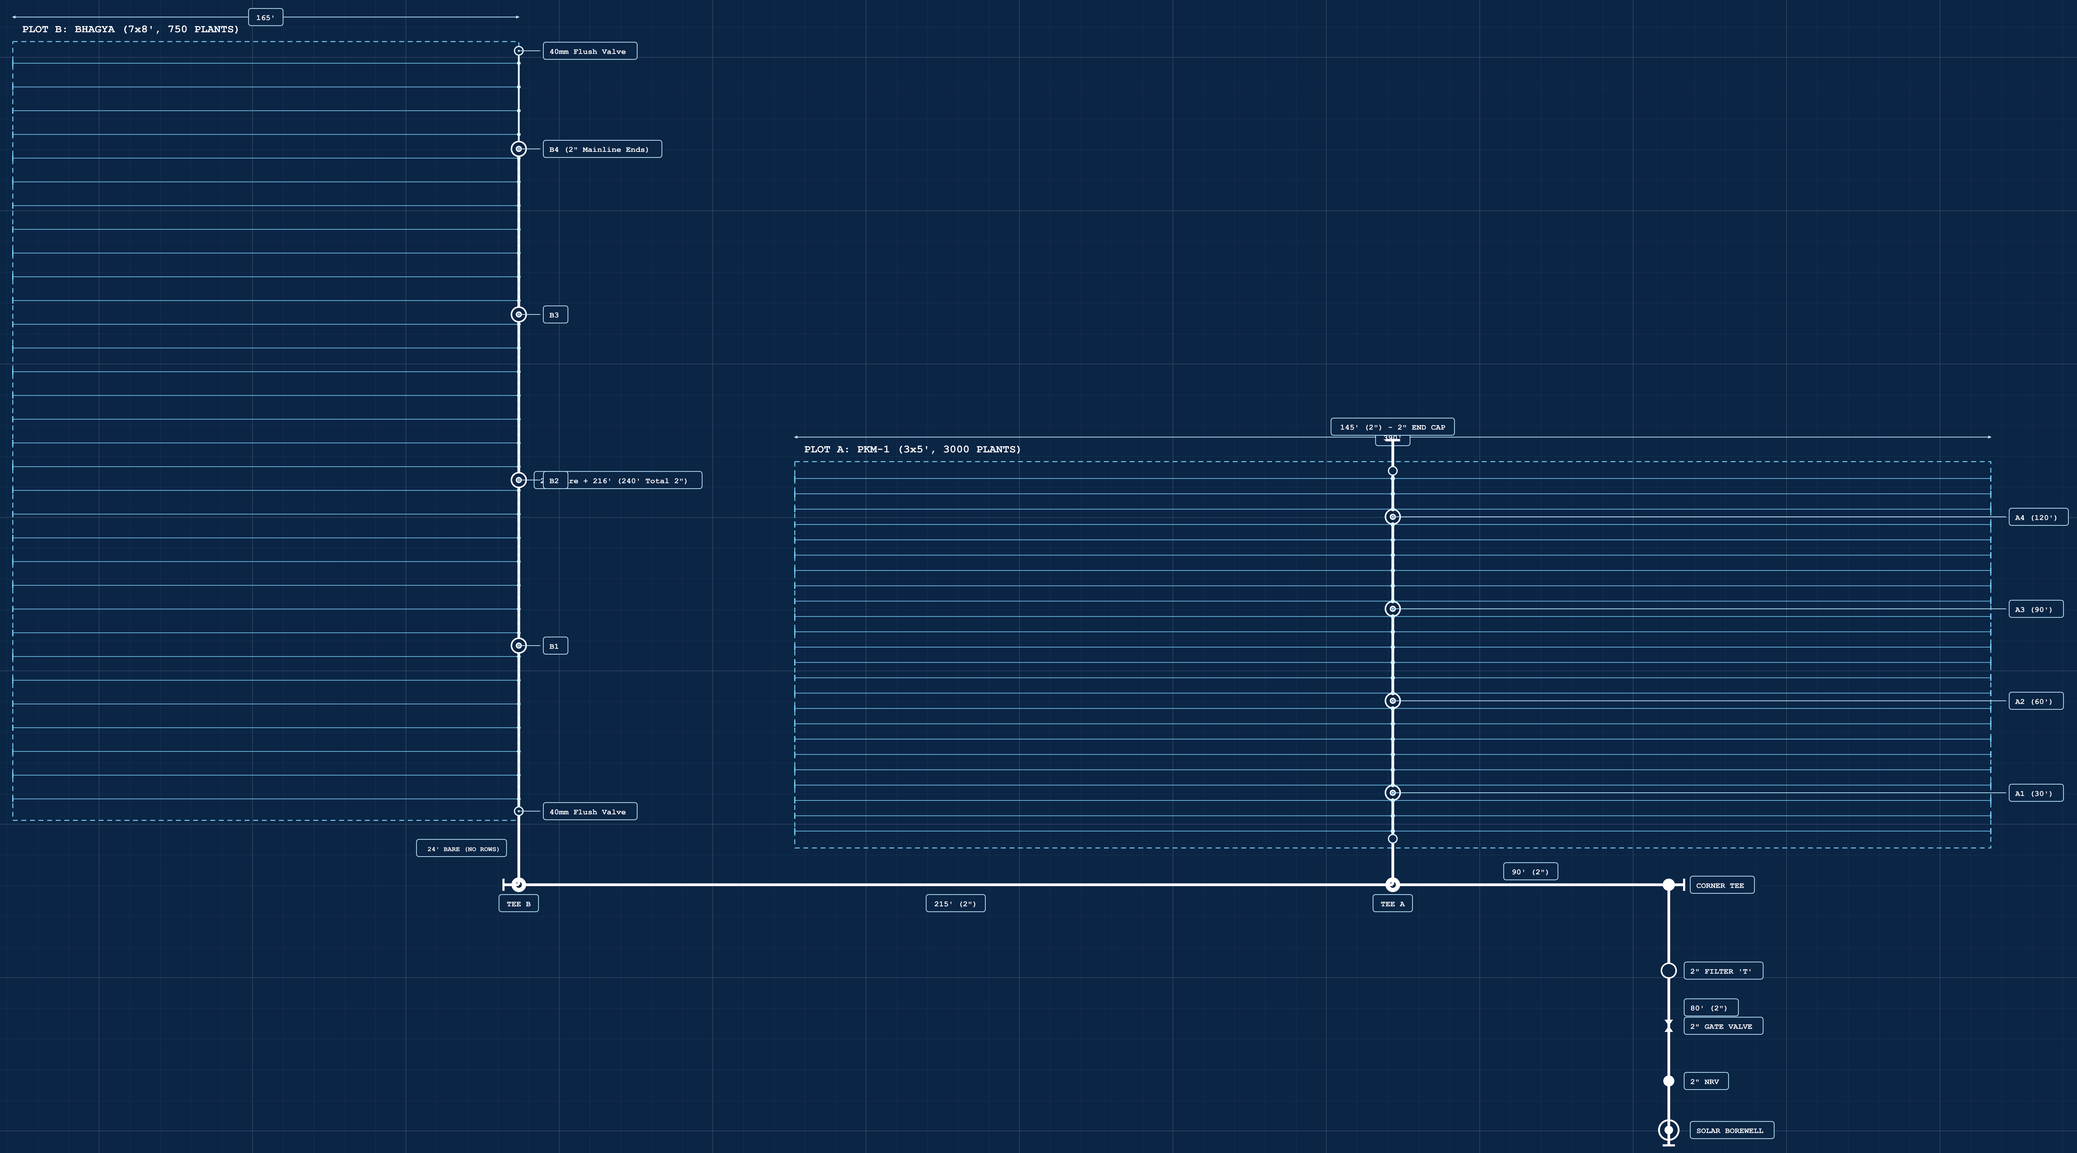


2-ACRE MORINGA DRIP LAYOUT | PLOT A: PKM-1 (3x5', 3000 PLANTS) | PLOT B: BHAGYA (7x8', 750 PLANTS) | SCALE: 1 FT = 5 PX

# 4-FOOT OVERHEAD DOUBLE-TEE RISER MANIFOLD — DETAIL ELEVATION

SHEET 2 OF 2 : SIDE-ELEVATION CROSS-SECTION (WAIST-HEIGHT DUAL CONTROLS)

PLOT A RISER: 2" RISER + 2x 50MM BALL VALVES + 1.5" DROPS TO 1.5" SUBLINE
PLOT B RISER: 2" RISER + 2x 40MM BALL VALVES + 1.25" DROPS TO 1.25" SUBLINE

SCALE: 1 FT = 60 PX

