
2-ACRE MORINGA IRRIGATION — MASTER BLUEPRINT

SHEET 1 OF 2 : TOP-DOWN MASTER FIELD BLUEPRINT

PLOT A RISER = 4' 2" RISER + 2x 50MM BALL VALVES + 15' N/S 1.5" SUBLINES + 2x 50MM FLUSH VALVES

PLOT B RISER = 4' 2" RISER + 2x 40MM BALL VALVES + 32' N/S 1.25" SUBLINES + 2x 40MM FLUSH VALVES

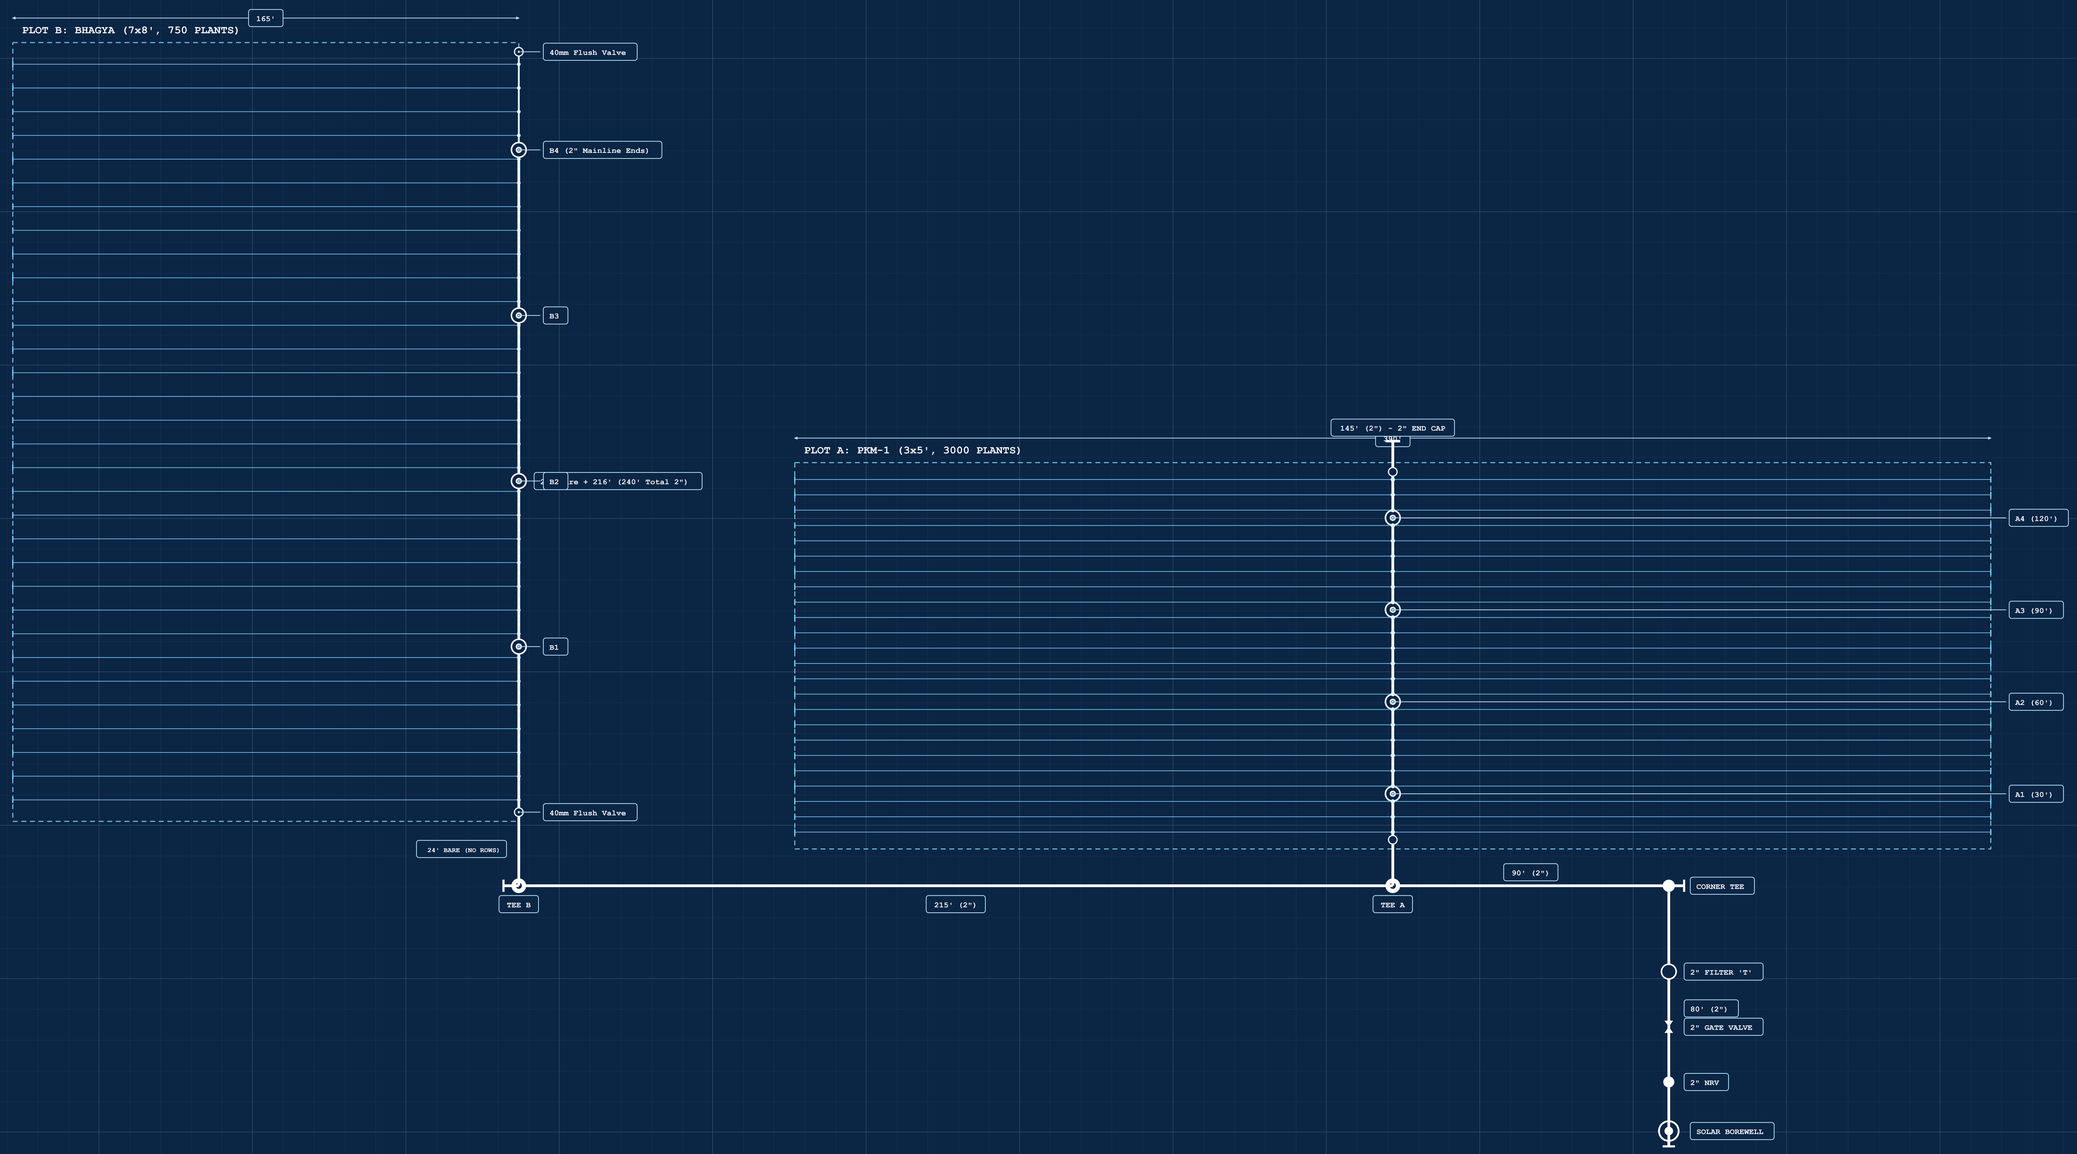

2-ACRE MORINGA DRIP LAYOUT | PLOT A: PKM-1 (3x5', 3000 PLANTS) | PLOT B: BHAGYA (7x8', 750 PLANTS) | SCALE: 1 FT = 5 PX