
4-FOOT OVERHEAD DOUBLE-TEE RISER MANIFOLD — DETAIL CROSS-SECTION

SIDE-ELEVATION LOOKING EAST • WAIST-HEIGHT VALVE CONTROLS • TRENCH DROP PROFILES

APPLIES TO RISERS A1–A4 (50MM BALL VALVES) & RISERS B1–B4 (40MM BALL VALVES) | SCALE: 1 FT = 60 PX

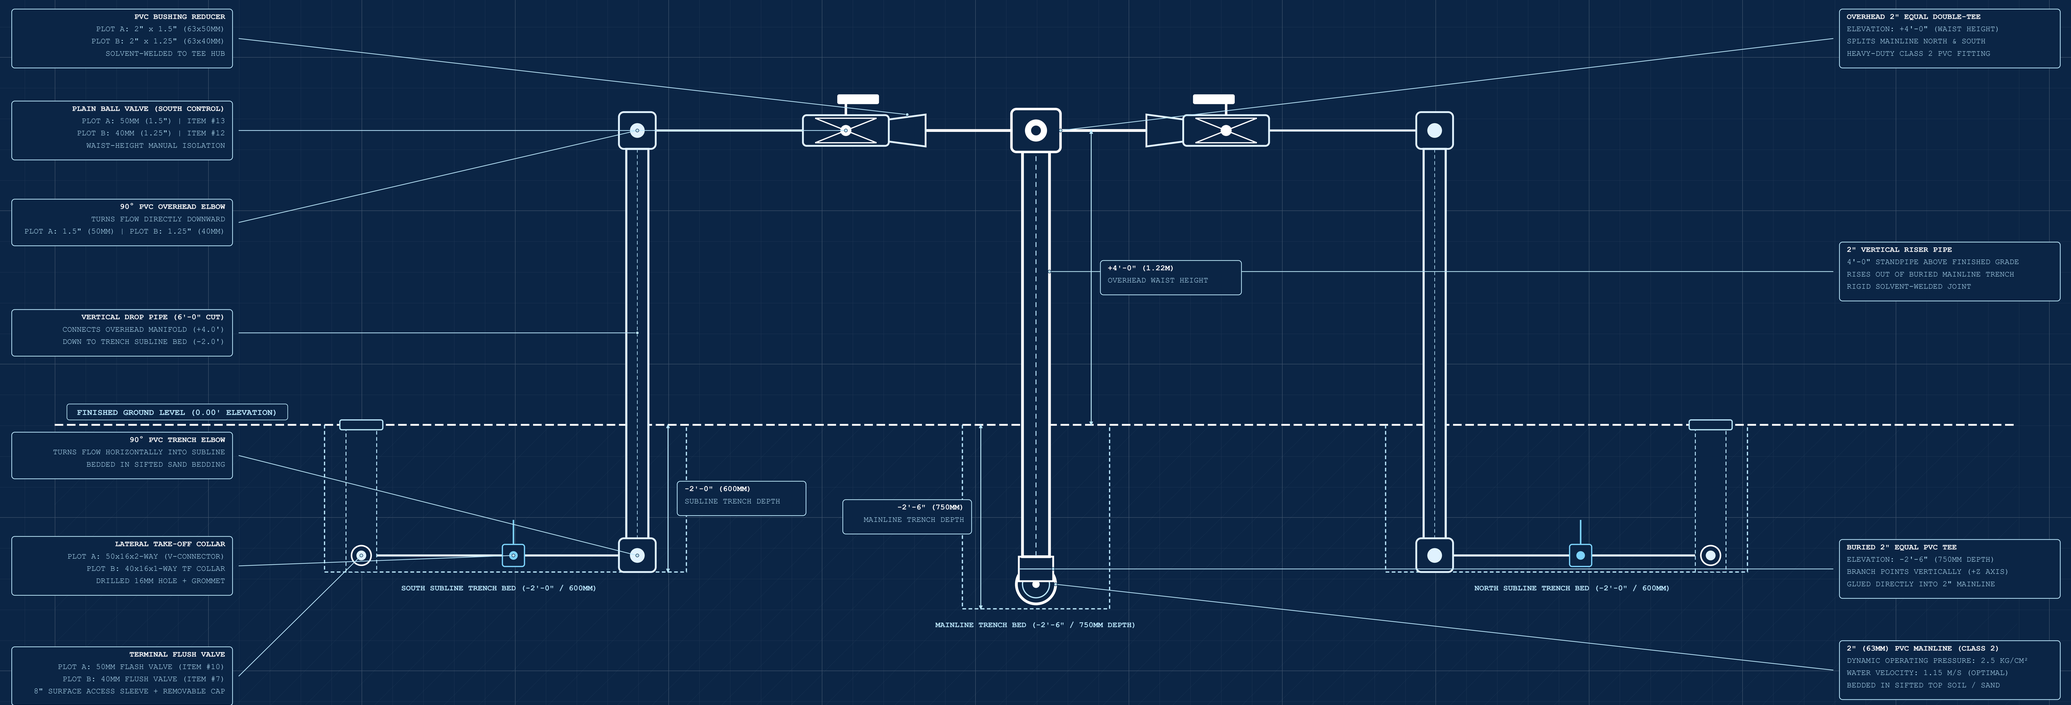

PROJECT & LOCATION:

2-ACRE MORINGA COMMERCIAL ORCHARD DRIP SYSTEM

DRAWING TITLE: **OVERHEAD RISER DETAIL**	PLOT A CONFIGURATION: **4 STATIONS (A1–A4 @ 30' CTRS)** 2x 50MM VALVES + 15' SUBLINES	PLOT B CONFIGURATION: **4 STATIONS (B1–B4 @ 64' CTRS)** 2x 40MM VALVES + 32' SUBLINES
OPERATIONAL HEIGHT: **+4'-0" (1.22M) WAIST LEVEL** ERGONOMIC ROTATION ACCESS	PLUMBING SPECIFICATION: **HEAVY SOLVENT CEMENT** 24-HR HYDROSTATIC CURE	TRENCH DRAINAGE: **SURFACE FLUSH SLEEVES** EASY MAINTENANCE ACCESS

SCALE:	DATE / STATUS:	CAD STANDARD:	SHEET NUMBER:
1 FT = 120 PX (1:10 DETAIL SCALE)	OCTOBER 2026 APPROVED FOR FIELD	IS 12786 / 4985 CROSS-SECTION DETAIL	SHEET 2 OF 2