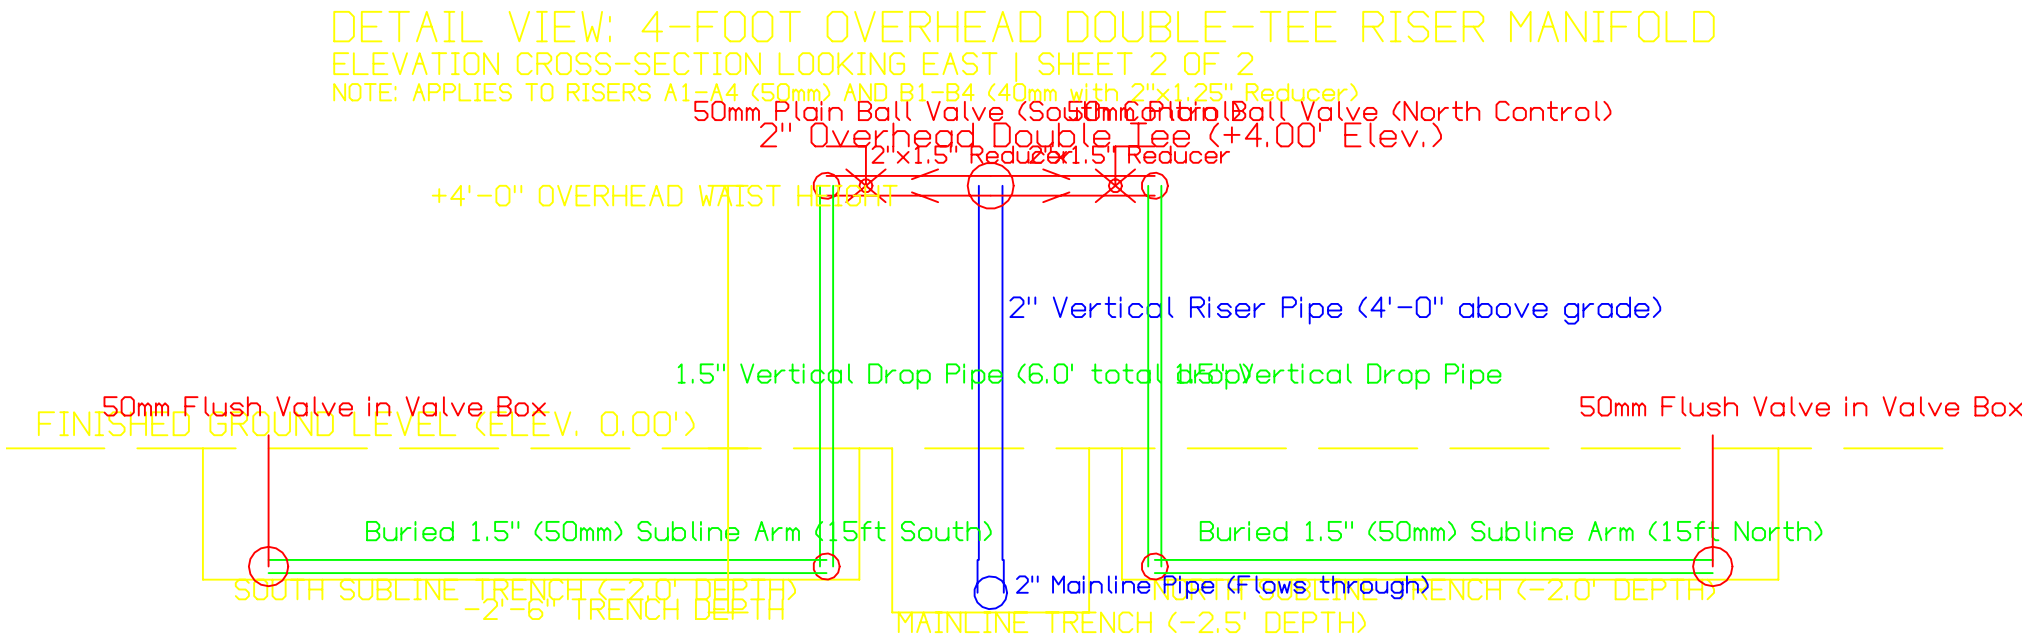
DETAIL VIEW: 4-FOOT OVERHEAD DOUBLE-TEE RISER MANIFOLD
ELEVATION CROSS-SECTION LOOKING EAST | SHEET 2 OF 2
NOTE: APPLIES TO RISERS A1–A4 (50mm) AND B1–B4 (40mm with 2"x1.25" Reducer)
50mm Plain Ball Valve (South Control)
50mm Plain Ball Valve (North Control)
2" Overhead Double Tee (+4.00' Elev.)
2"x1.5" Reducer
2"x1.5" Reducer
+4'-0" OVERHEAD WAIST HEIGHT
2" Vertical Riser Pipe (4'-0" above grade)
1.5" Vertical Drop Pipe (6.0' total drop)
1.5" Vertical Drop Pipe
50mm Flush Valve in Valve Box
50mm Flush Valve in Valve Box
FINISHED GROUND LEVEL (ELEV. 0.00')
Buried 1.5" (50mm) Subline Arm (15ft South)
Buried 1.5" (50mm) Subline Arm (15ft North)
2" Mainline Pipe (Flows through)
SOUTH SUBLINE TRENCH (-2.0' DEPTH)
-2'-6" TRENCH DEPTH
NORTH SUBLINE TRENCH (-2.0' DEPTH)
MAINLINE TRENCH (-2.5' DEPTH)